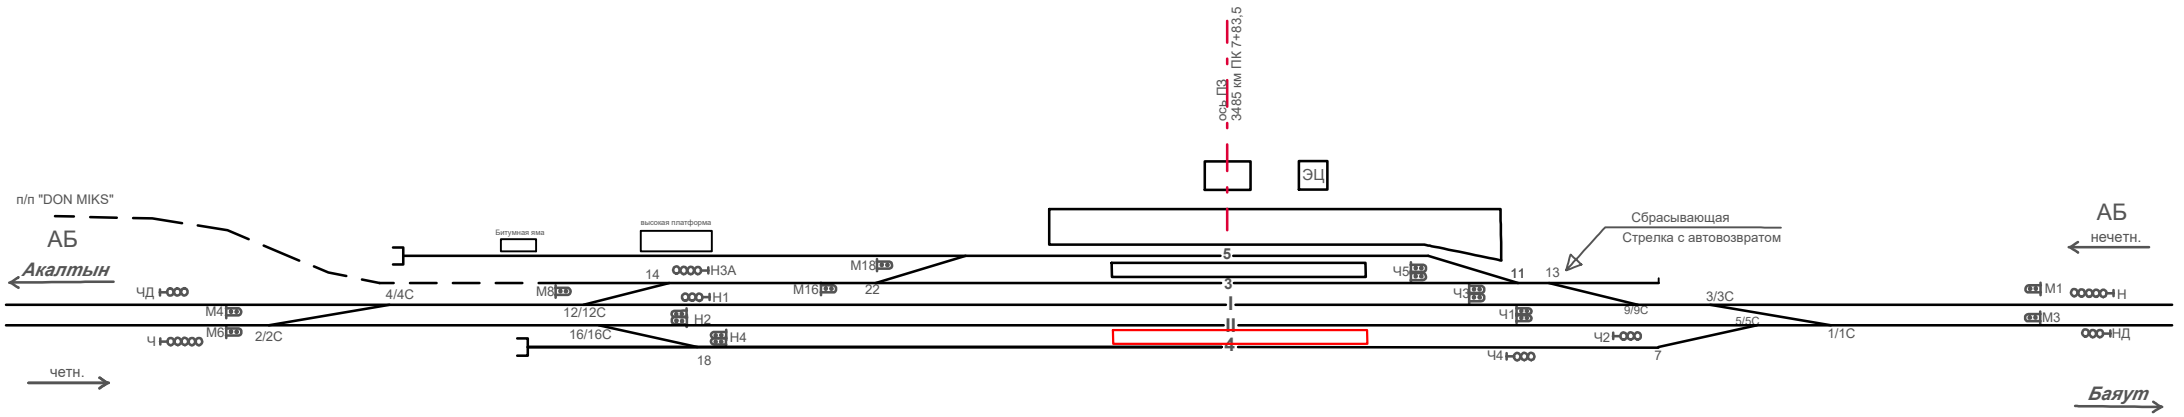
ст. ГУЛИСТАН


ось ПЗ
3485 км ПК 7+83.5
ЭЦ
п/п "DON MIKS"
АБ
Акалтын
Битумная яма
высокая платформа
Сбрасывающая
Стрелка с автовозвратом
АБ
нечетн.
ЧД
М4
М6
Ч
2/2С
4/4С
М8
14
Н3А
12/12С
Н1
Н2
16/16С
Н4
18
М18
М16
22
5
3
1
II
4
Ч5
Ч3
Ч1
Ч2
Ч4
11
13
9/9С
7
3/3С
5/5С
1/1С
М1
Н
М3
НД
четн.
Баяут