ст. ЗАРБДАР

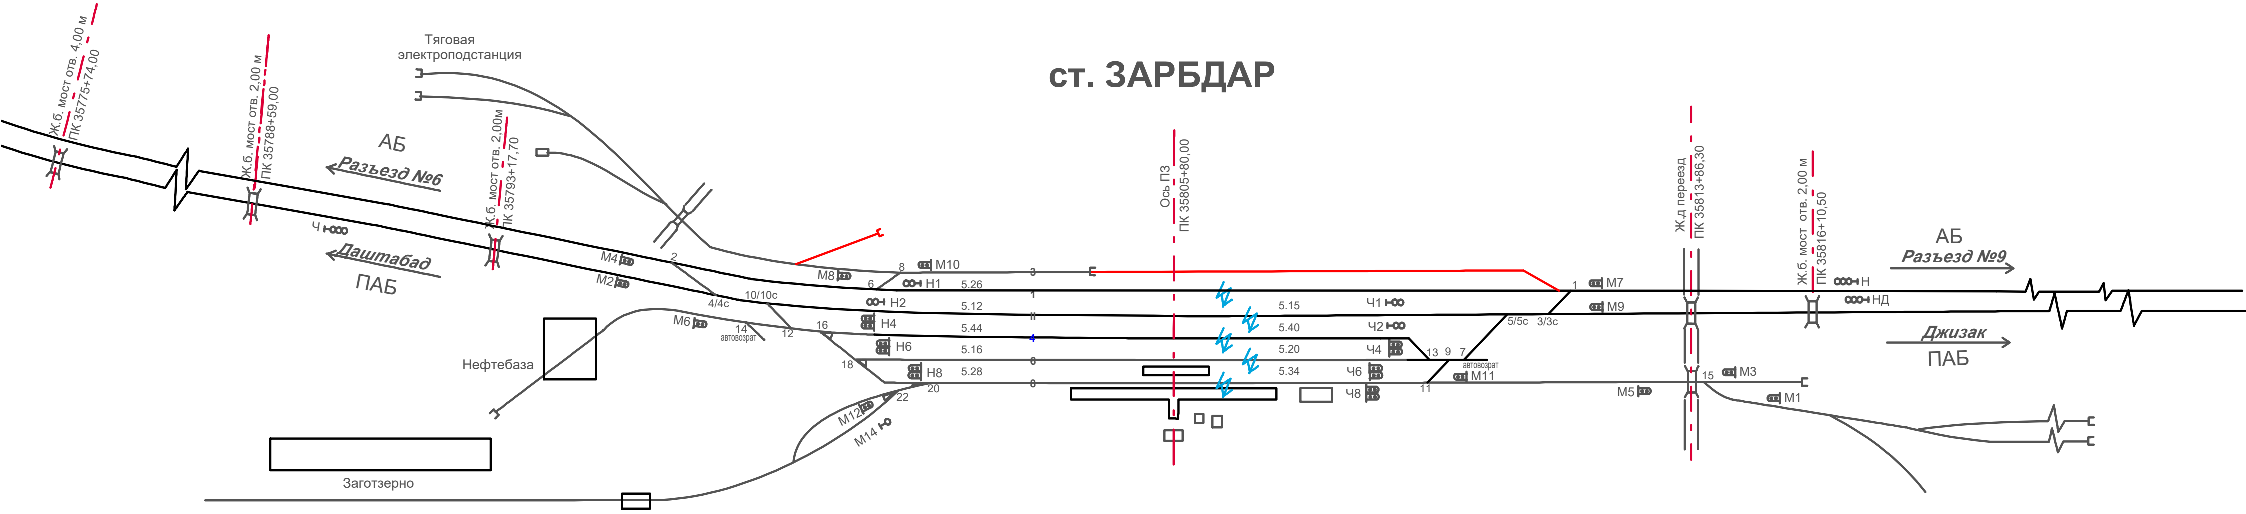
Ж.б. мост отв. 4,00 м
ПК 35775+74,00
Ж.б. мост отв. 2,00 м
ПК 35788+59,00
Тяговая
электроподстанция
АБ
Разъезд №6
Ж.б. мост отв. 2,00м
ПК 35793+17,70
Ч
Даштабад
ПАБ
М4
М2
2
4/4с
10/10с
М6
14
автовозрат
12
16
18
Нефтебаза
Заготзерно
М8
8
М10
6
Н1
5.26
3
1
Н2
5.12
II
Н4
5.44
4
Н6
5.16
6
Н8
5.28
8
20
22
М12
М14
Ось ПЗ
ПК 35805+80,00
5.15
Ч1
5.40
Ч2
5.20
Ч4
5.34
Ч6
Ч8
13
9
7
автовозрат
М11
11
5/5с
3/3с
1
М7
М9
Ж.д переезд
ПК 35813+86,30
15
М5
М3
М1
Ж.б. мост отв. 2,00 м
ПК 35816+10,50
Н
НД
АБ
Разъезд №9
Джизак
ПАБ