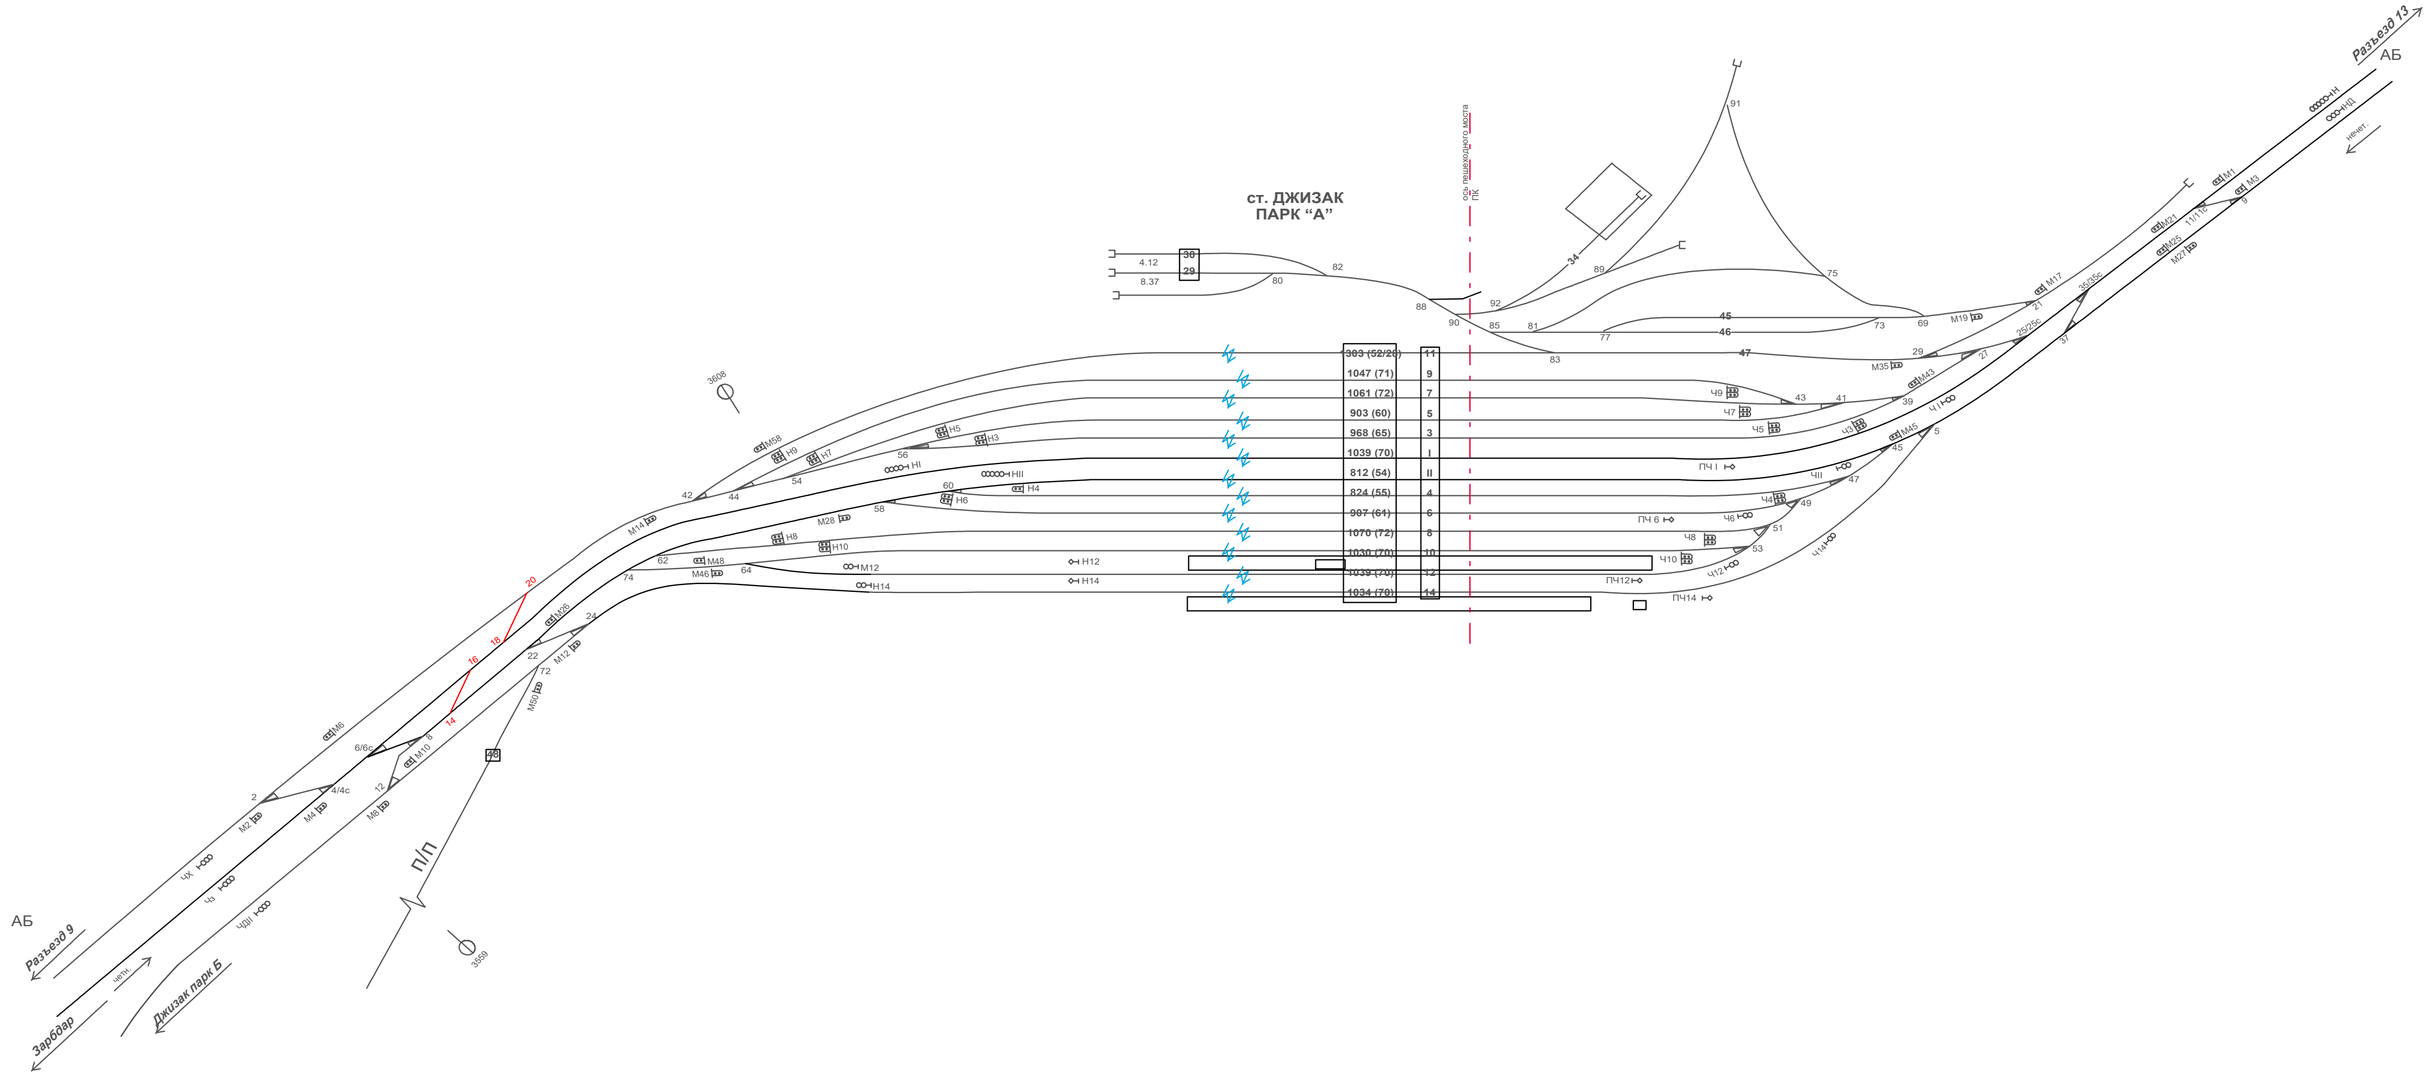

ст. ДЖИЗАК
ПАРК "А"
ось пешеходного моста ПК
303 (52/26) 11
1047 (71) 9
1061 (72) 7
903 (60) 5
968 (65) 3
1039 (70) I
812 (54) II
824 (55) 4
907 (61) 6
1070 (72) 8
1030 (70) 10
1039 (70) 12
1034 (70) 14
4.12
8.37
АБ
Разъезд 9
Зарбдар
Джизак парк Б
Разъезд 13
п/п
3608
3559
ПЧ I
ПЧ 6
ПЧ12
ПЧ14
нечет.