ст. ЗАРАВШАН

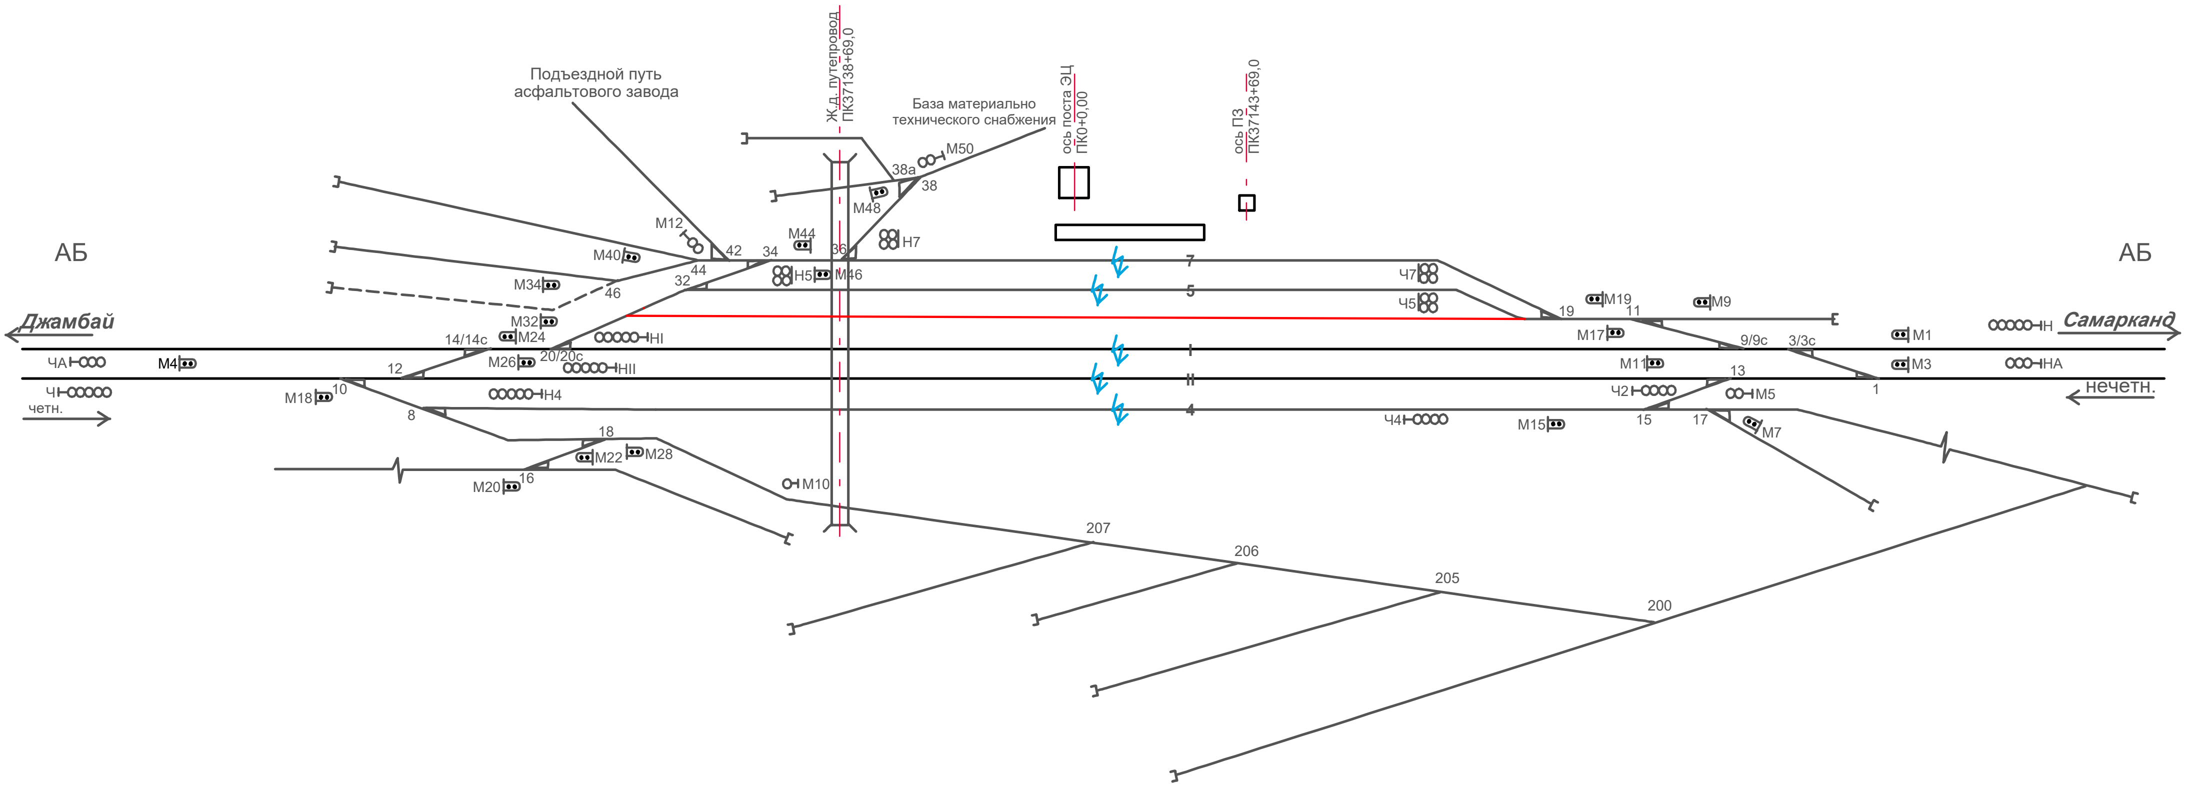

АБ
АБ
Джамбай
Самарканд
четн.
нечетн.
Подъездной путь асфальтового завода
Ж.д. путепровод ПК37138+69,0
База материально технического снабжения
ось поста ЭЦ ПК0+0,00
ось ПЗ ПК37143+69,0
M50
38а
38
M48
M12
M40
M44
H7
42
34
36
44
32
H5
M46
M34
46
M32
M24
14/14с
HI
20/20с
M26
HII
ЧА
M4
12
Ч
M18
10
H4
8
18
M22
M28
M20
16
M10
7
5
I
II
4
Ч7
Ч5
19
M19
11
M9
M17
9/9с
3/3с
M1
H
M11
M3
HA
13
1
Ч2
M5
Ч4
M15
15
17
M7
207
206
205
200