ст. ДАШТОБАД

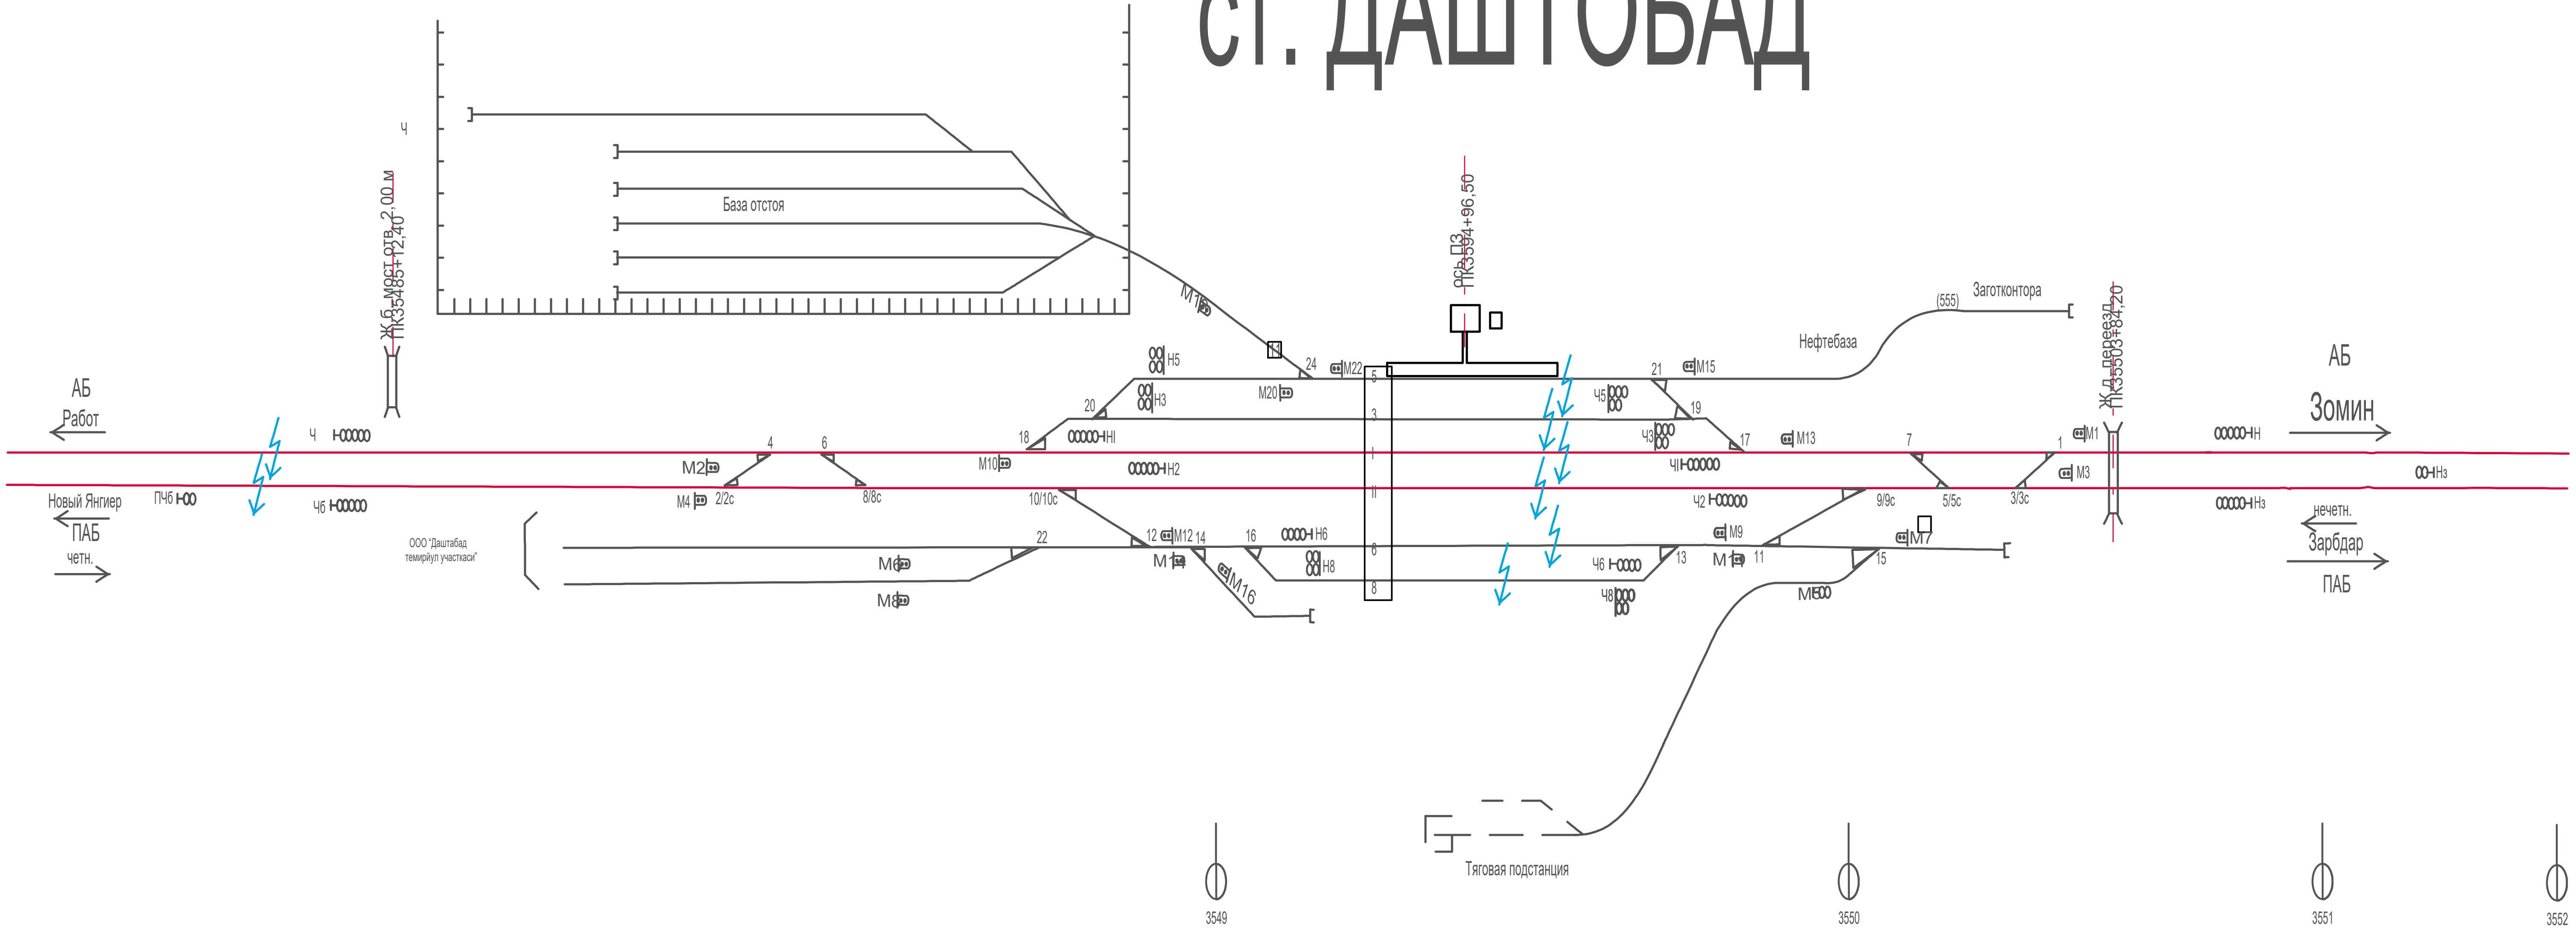
Ж.б. мост отв. 2,00 м
ПК35485+12,40
Ч
База отстоя
М18
ось ПЗ
ПК3594+96,50
Заготконтора
(555)
Нефтебаза
Ж.д. переезд
ПК35503+84,20
АБ
Работ
Новый Янгиер
ПАБ
четн.
ПЧб
Ч
Чб
ООО "Даштабад темирйул участкаси"
М2
М4
2/2с
4
6
8/8с
М6
М8
18
20
22
10/10с
М10
НI
Н2
Н3
Н5
12
М12
14
М14
16
М16
Н6
Н8
24
М20
М22
5
3
I
II
6
8
Ч5
Ч3
ЧI
Ч2
Ч6
Ч8
21
М15
19
17
М13
13
М9
М11
11
15
М5
М7
9/9с
7
5/5с
3/3с
1
М1
М3
Н
Нз
АБ
Зомин
нечетн.
Зарбдар
ПАБ
Тяговая подстанция
3549
3550
3551
3552