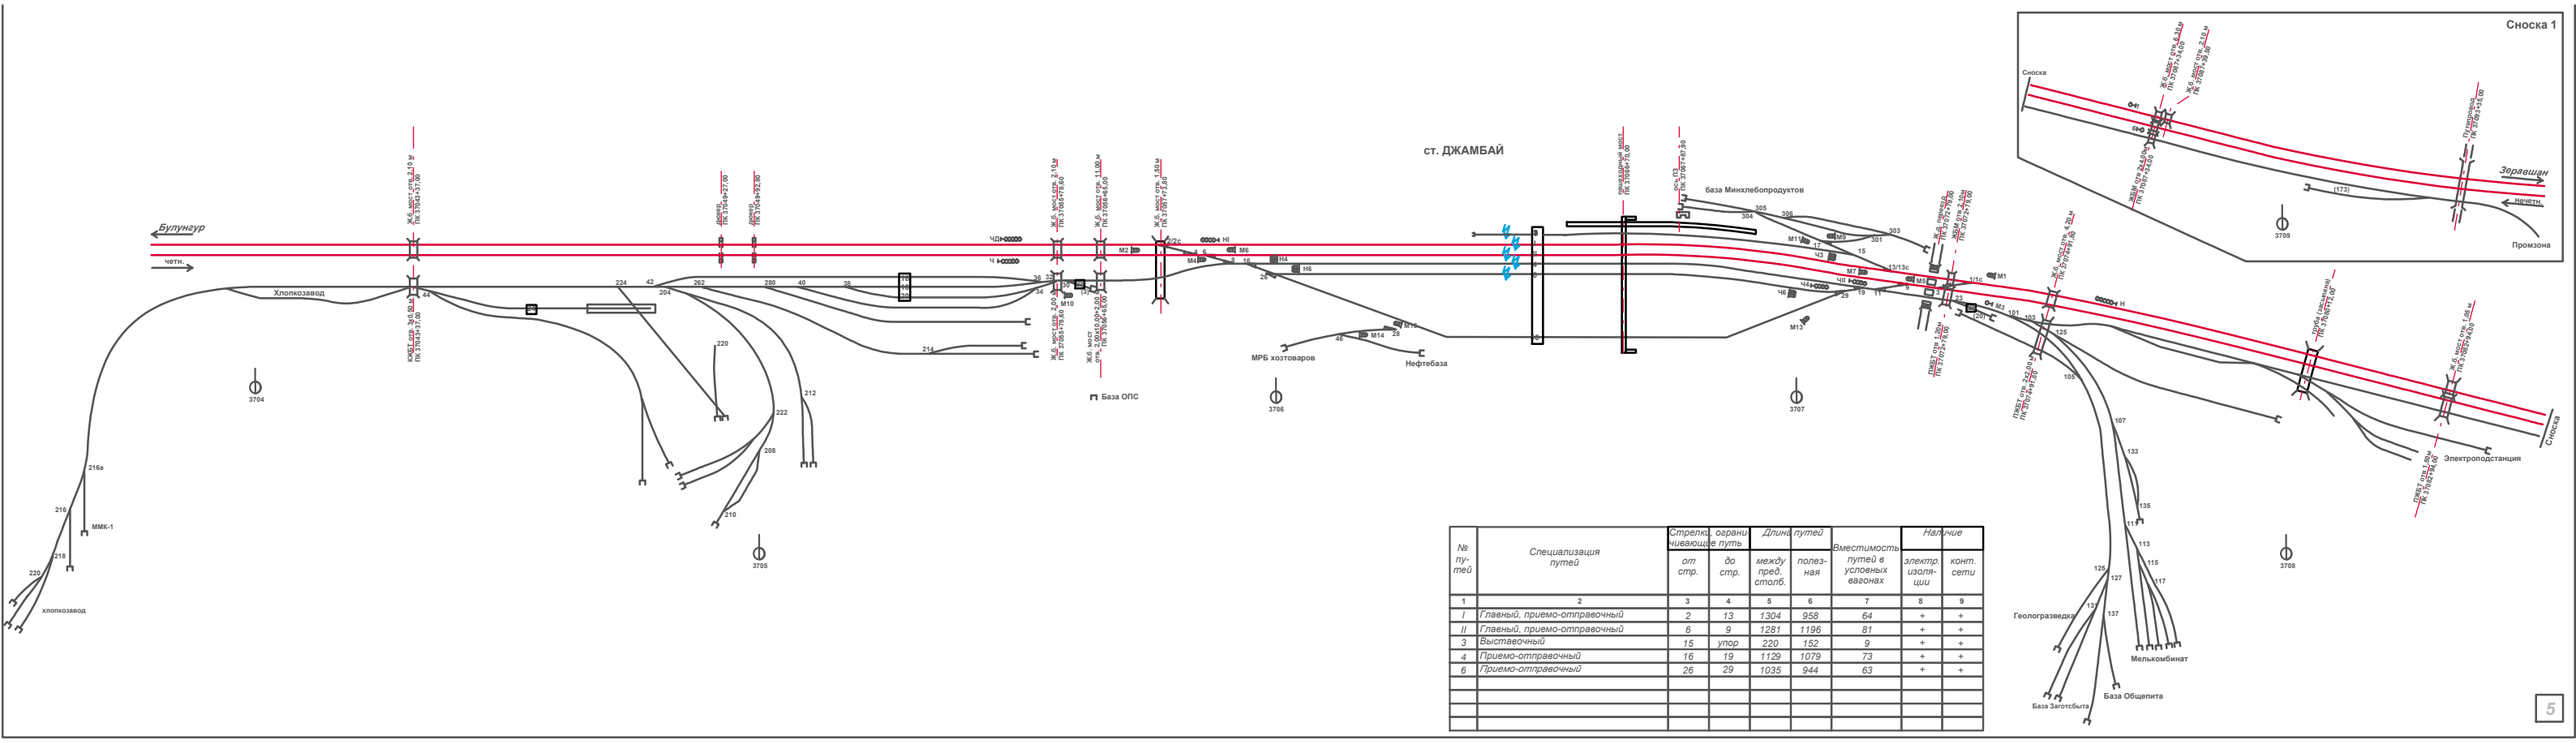


№ пу-тей	Специализация путей	Стрелки, ограничивающие путь		Длина путей		Вместимость путей в условных вагонах	Наличие	
		от стр.	до стр.	между пред. столб.	полез-ная		электр. изоли-ции	конт. сети
1	2	3	4	5	6	7	8	9
I	Главный, приемо-отправочный	2	13	1304	958	64	+	+
II	Главный, приемо-отправочный	6	9	1281	1196	81	+	+
3	Выставочный	15	упор	220	152	9	+	+
4	Приемо-отправочный	16	19	1129	1079	73	+	+
6	Приемо-отправочный	26	29	1035	944	63	+	+