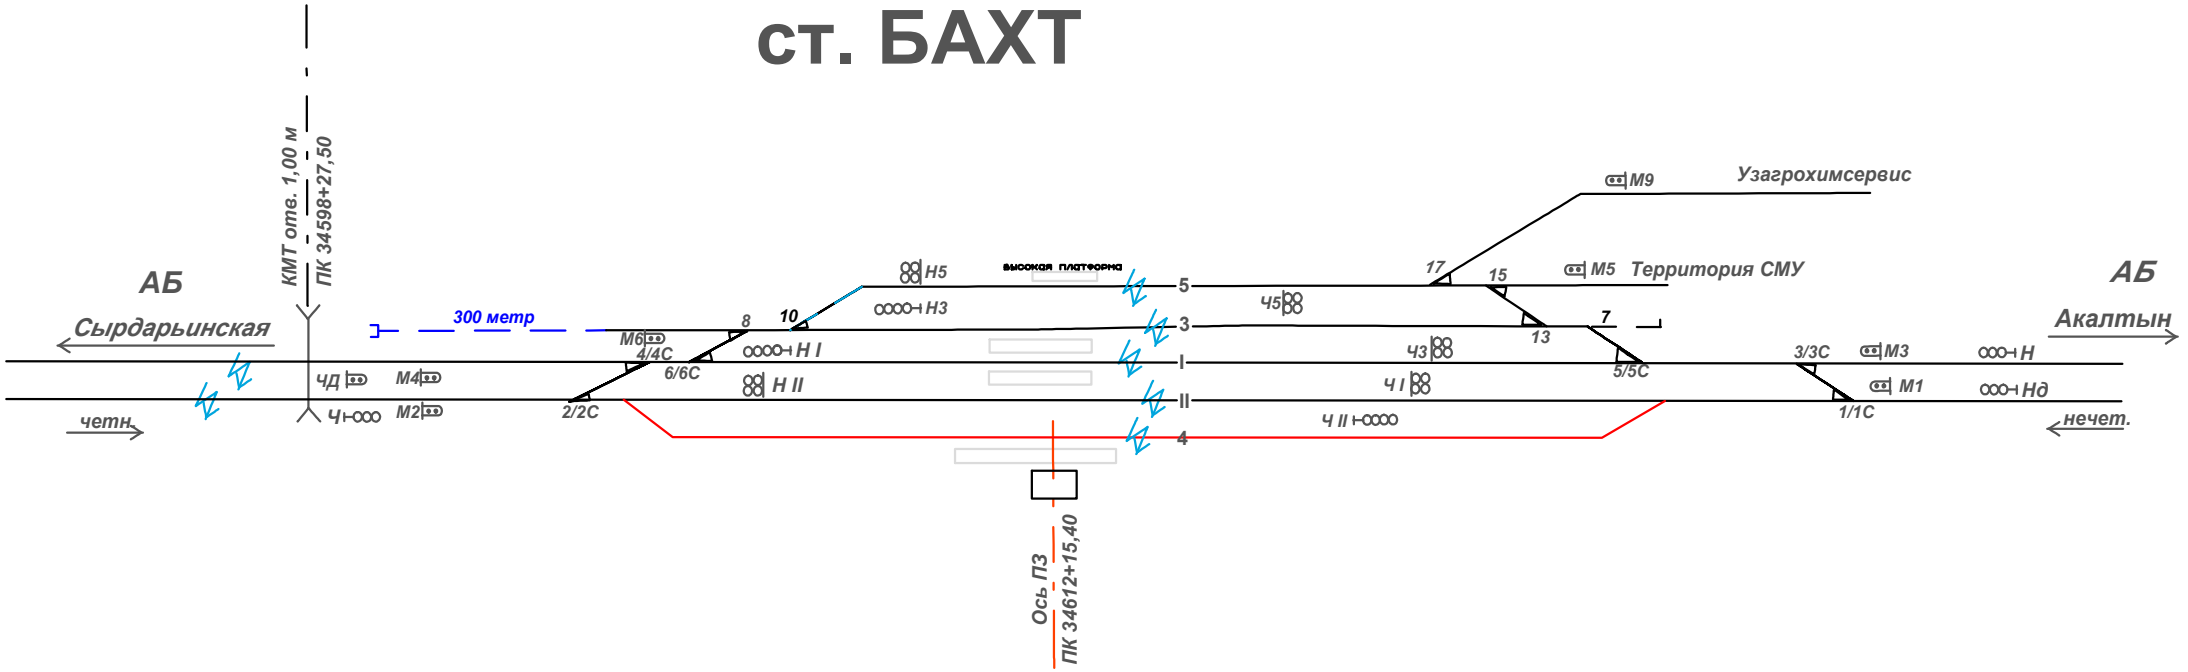
ст. БАХТ


АБ
Сырдарьинская
четн.
КМТ отв. 1,00 м
ПК 34598+27,50
300 метр
ЧД
Ч
М4
М2
М6
4/4С
6/6С
2/2С
8
10
Н5
Н3
Н I
Н II
высокая платформа
5
3
I
II
4
Ч5
Ч3
Ч I
Ч II
17
15
13
7
5/5С
М9
Узагрохимсервис
М5
Территория СМУ
3/3С
М3
Н
М1
Нд
1/1С
АБ
Акалтын
нечет.
Ось ПЗ
ПК 34612+15,40