Ст. Акалтын

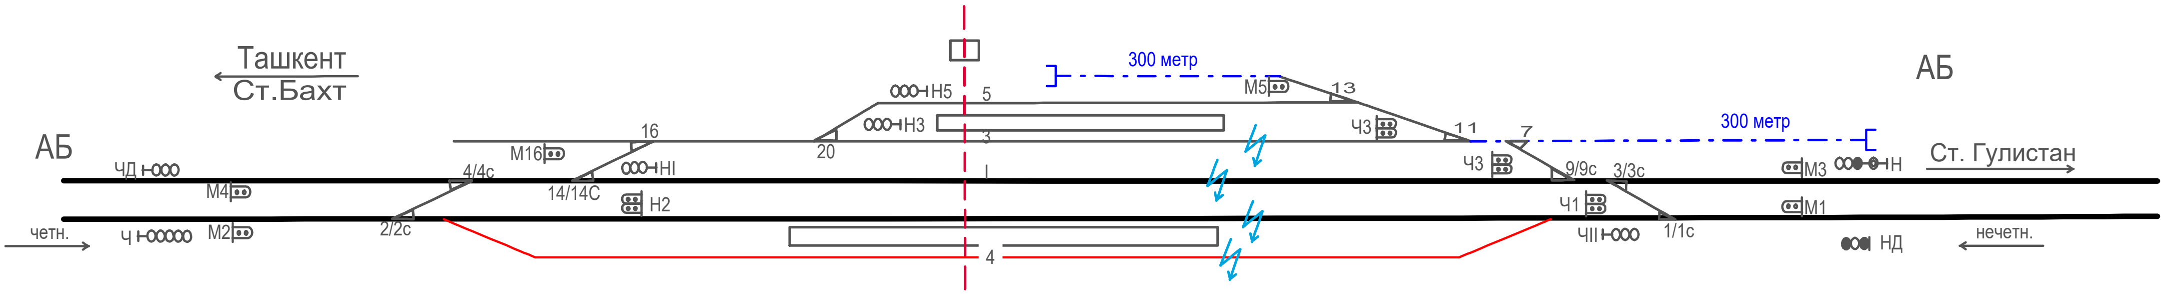
Ташкент
Ст.Бахт
АБ
ЧД
М4
четн.
Ч
М2
2/2с
4/4с
М16
16
14/14С
НI
Н2
20
Н5
5
Н3
3
I
4
300 метр
М5
13
Ч3
11
7
Ч3
9/9с
3/3с
Ч1
ЧII
1/1с
300 метр
АБ
М3
Н
Ст. Гулистан
М1
НД
нечетн.